
Sala de Estar

<u>Janelas</u>

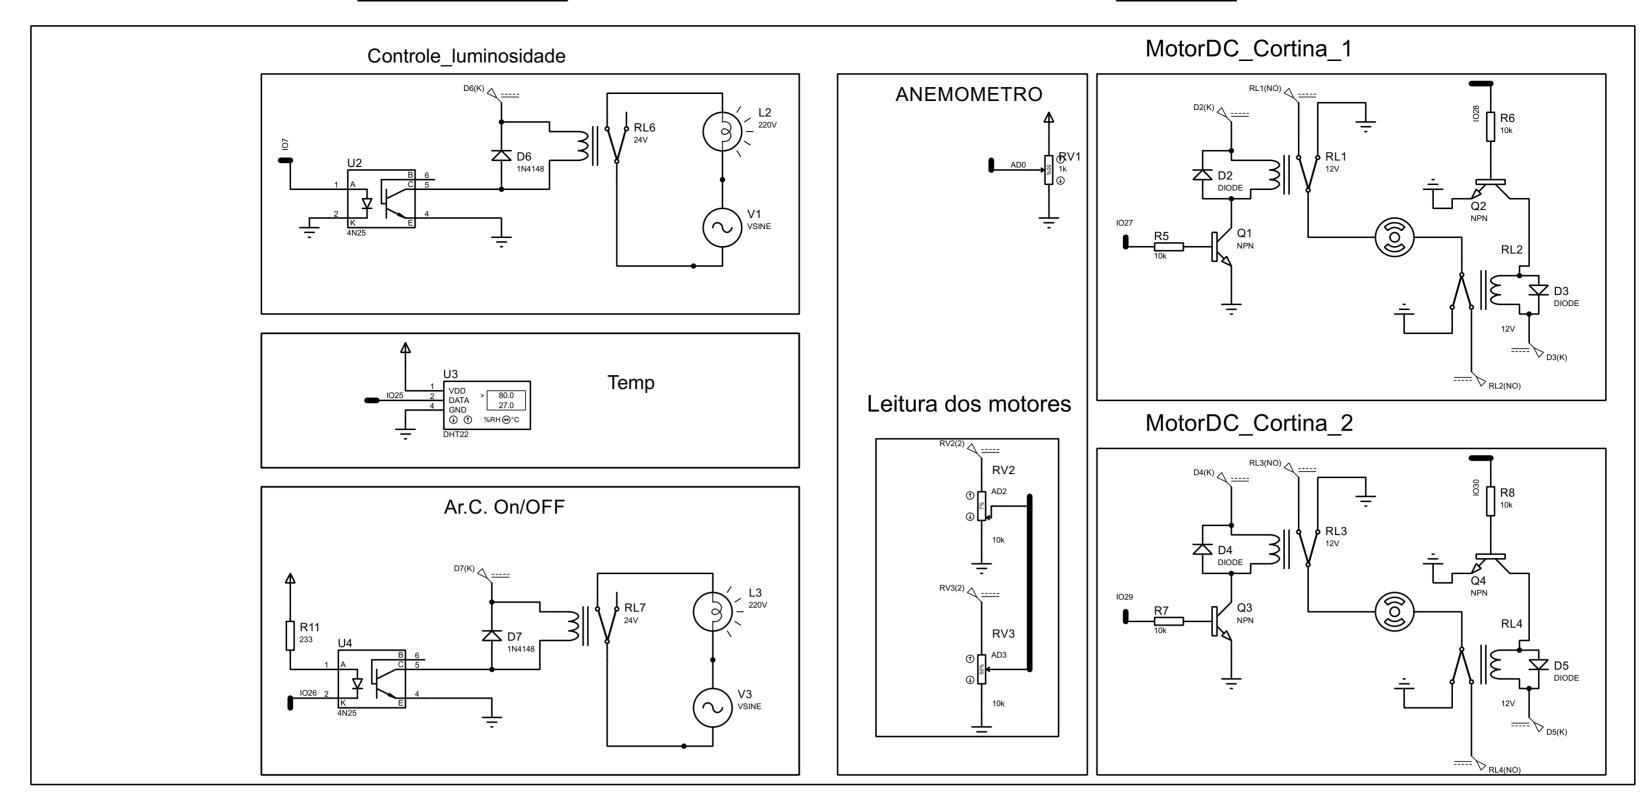

Entrada Principal

